

ESCALA 1:100

## MARQUES LONGITUDINALS DISCONTÍNUES

M-1.3 PER A VIES AMB V.≤60 Km/h i VORAL<1,5m.

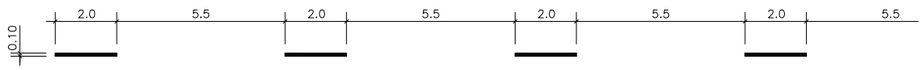


M-1.7 PER A VIES AMB V.≤60 Km/h i VORAL<1,5m.

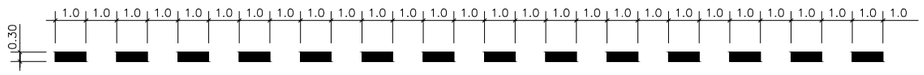


## MARQUES LONGITUDINALS CONTÍNUES

M-2.2 PER A SEPARACIÓ DE SENTITS EN CALÇADA DE DOS O TRES CARRILS




M-2.3B PER A SEPARACIÓ DE SENTITS EN CALÇADA ÚNICA DE TRES O MES CARRILS




M-2.4 PER A LIMIT DE CALÇADA, VORAL O LIMIT DE ILLETA INFRANQUEJABLE




M-2.6 PER A SEPARACIÓ DE CARRIL CENTRAL D'ESPERA




## MARQUES TRANSVERSALS

M-4.1 LÍNIA DE DETENCIÓ





M-4.2 LÍNIA DE CEDIU EL PAS





## MARQUES LONGITUDINALS DE PROHIBICIÓ DE PARADA o ESTACIONAMENT

M-7.9 LÍNIA EN ZIGA-ZAGA

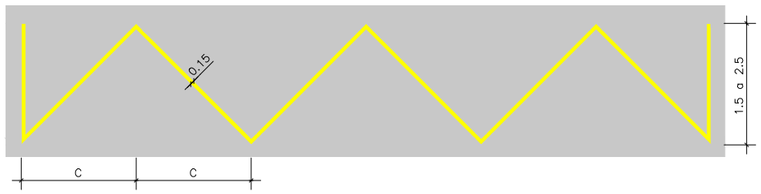



## MARCA COMENÇAMENT CARRIL BUS M-7.6

S/E

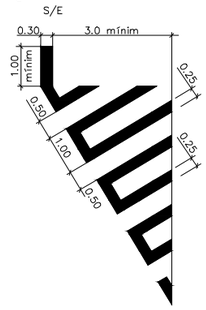


S/E

M-4.3

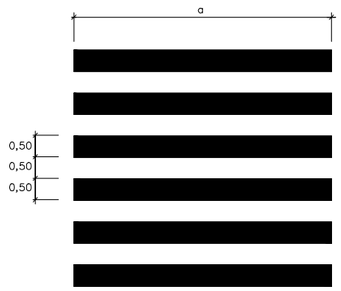


## CARRIL BICICLETA


M-6.10b

ESCALA 1:20



ESCALA 1:20


M-6.4 VIA AMB V.M. ≤ 60 Km/h

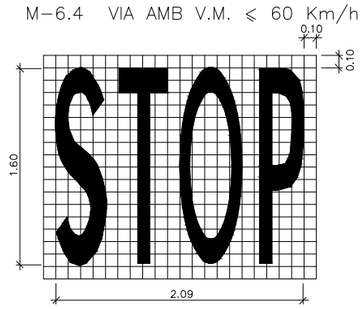


## BUS


ESCALA 1:20

M-6.2 VIA AMB V.M. ≤ 60 Km/h

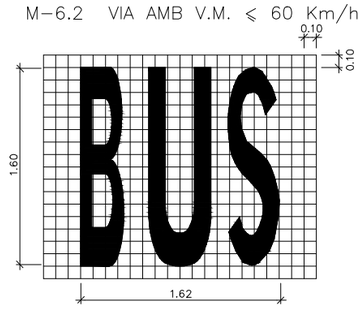


ESCALA 1:20

M-6.5 VIA AMB V.M. < 60 Km/h

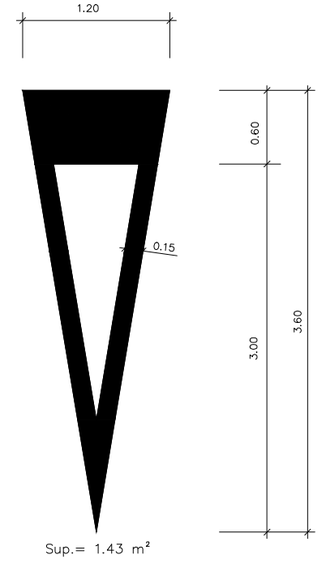


Sup.= 1.43 m²

## CEDIU EL PAS CARRIL BICI


ESCALA 1:20




## FLETXES DE DIRECCIÓ O SELECCIÓ DE CARRILS

S/E


M-5.2a

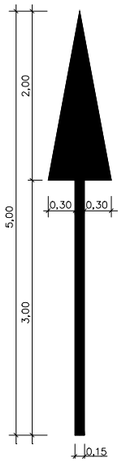


M-5.2c

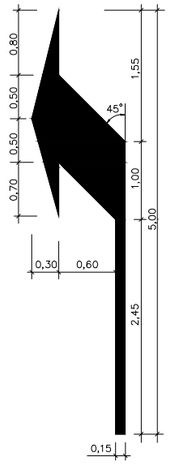



M-5.4b

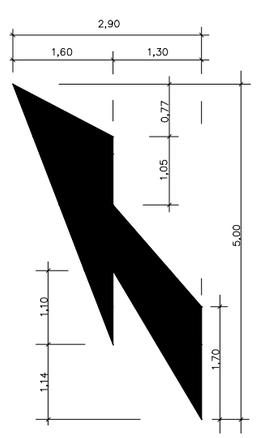


## ZEBREJAT ILLETES


S/E

CIRCULACIÓ EN DOBLE SENTIT (M-7.2a)

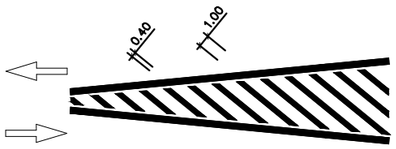



CIRCULACIÓ EN SENTIT ÚNIC

DIVERGENT (M-7.2b)

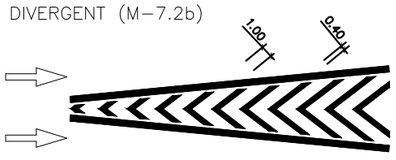


CONVERGENT (M-7.2c)

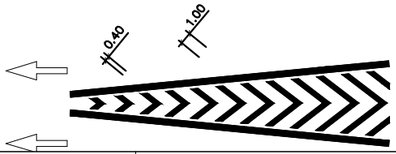


Ajuntament de Mataró

Servei de Mobilitat

CAP SERVEI

ENG./ARQ.

T.E DELINEANT JOAN BAENA

TÍTOL DEL PROJECTE

PROJECTE ...

NOM DEL PLÀNOL

DETALLS SENYALITZACIÓ HORITZONTAL

ARXIU: ..\SENYALS\2026\SIMBOLOGIA.DWG

ESCALA SENSE ESCALA

DATA

NÚMERO 1/6